



1 Planta de techo

1 : 50

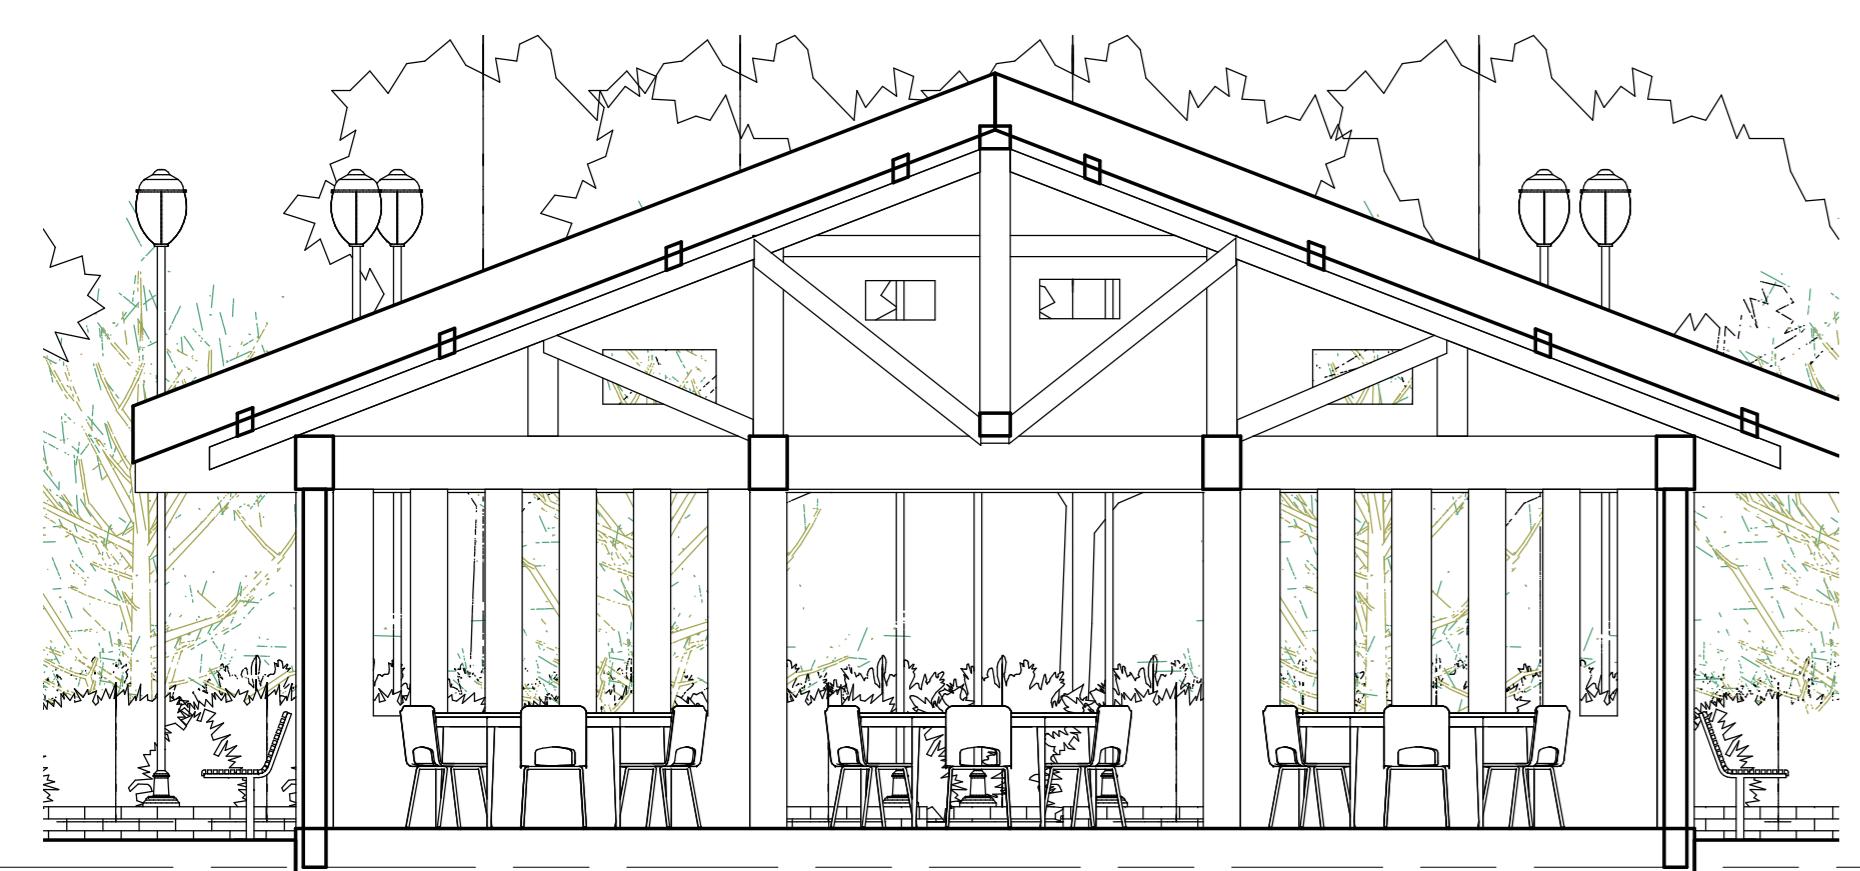

2 Detalle de techo

1 : 50

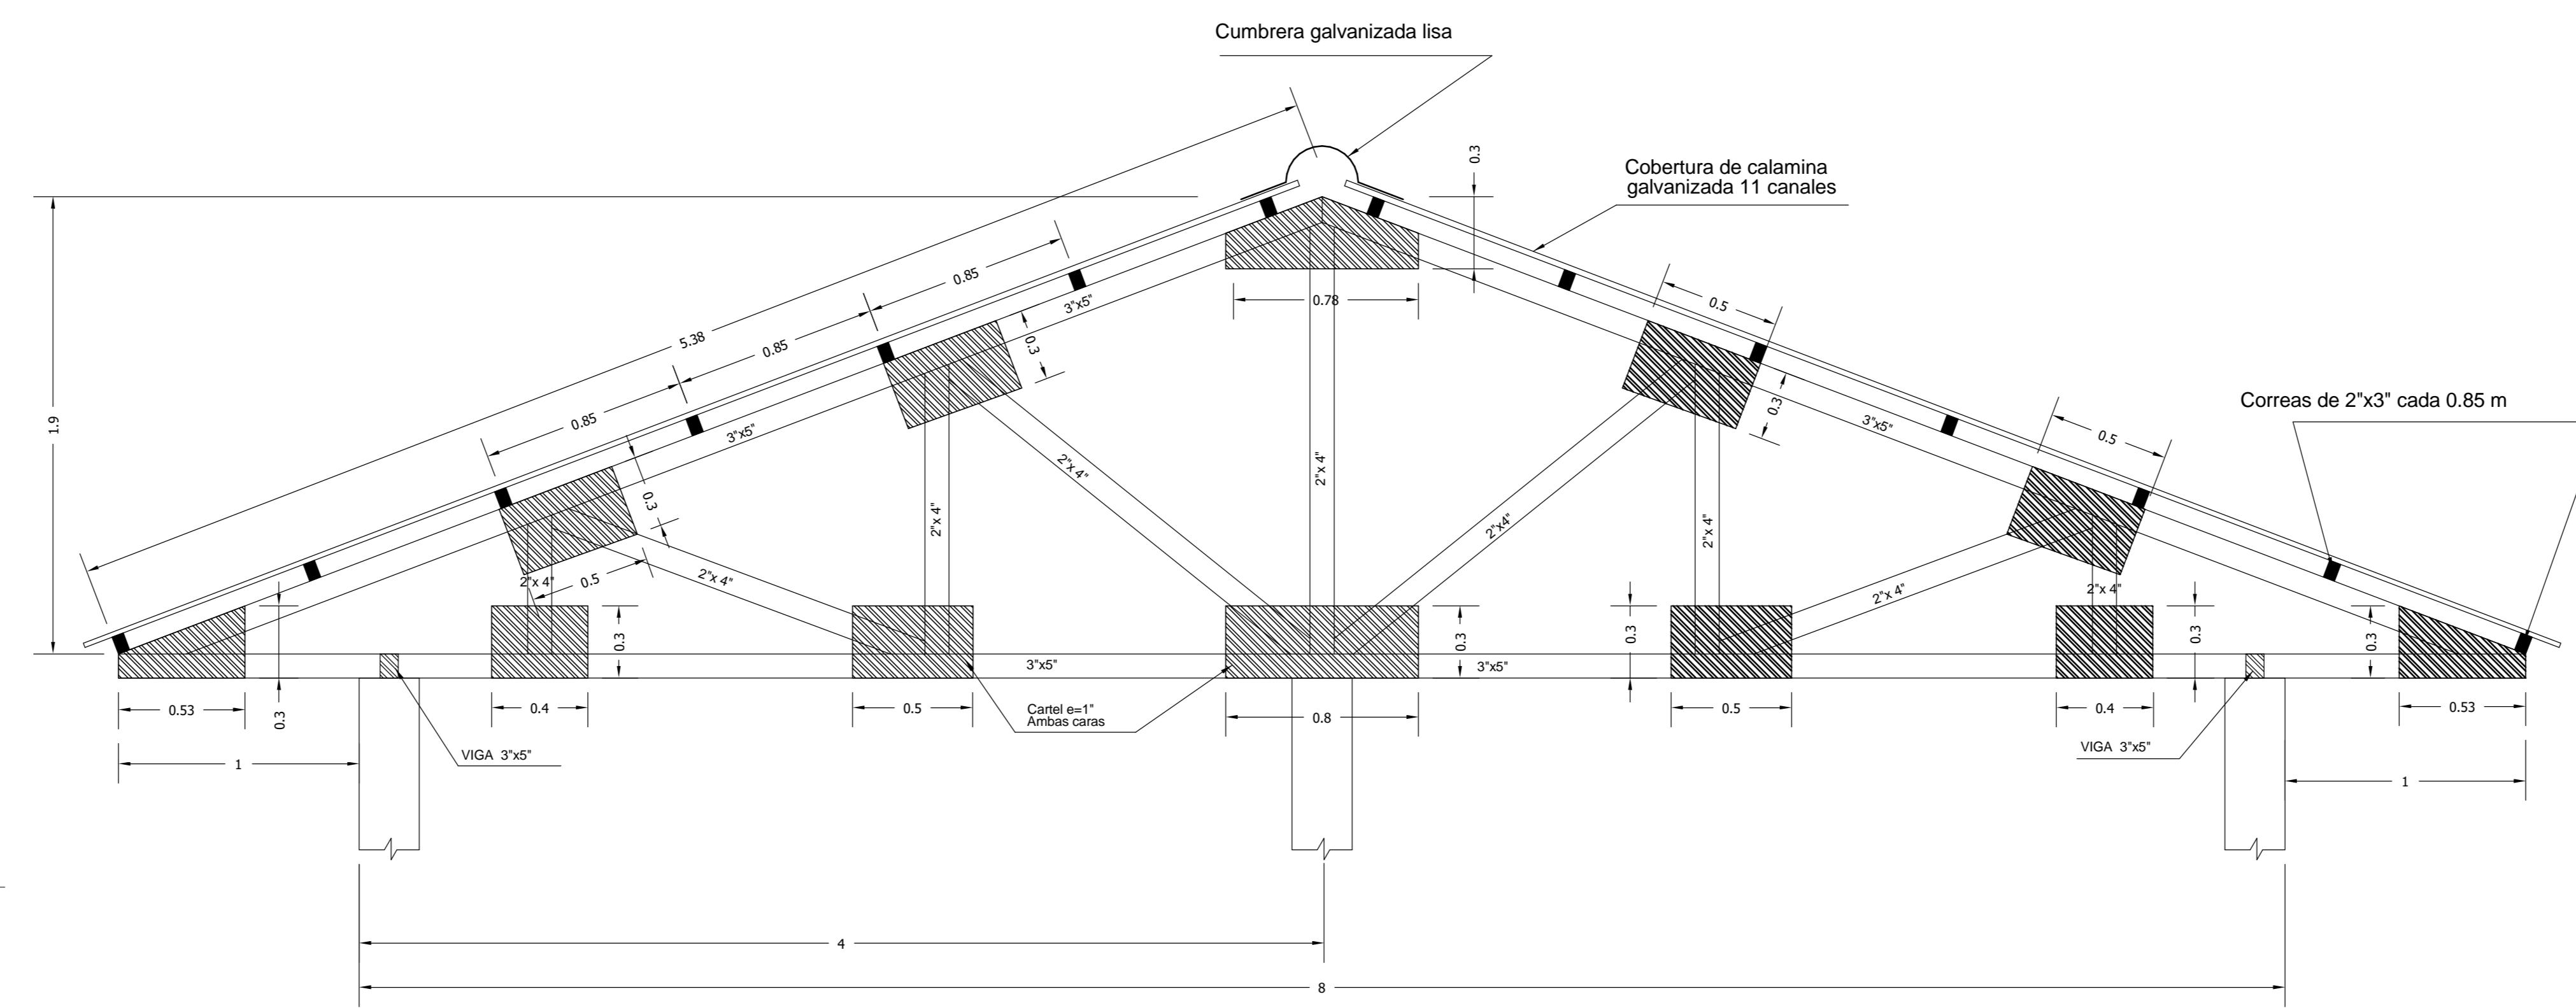


## TIJERAL DE MADERA TIPICO T1

Escala : 1 / 20

3 Tijereta de madera

1 : 20

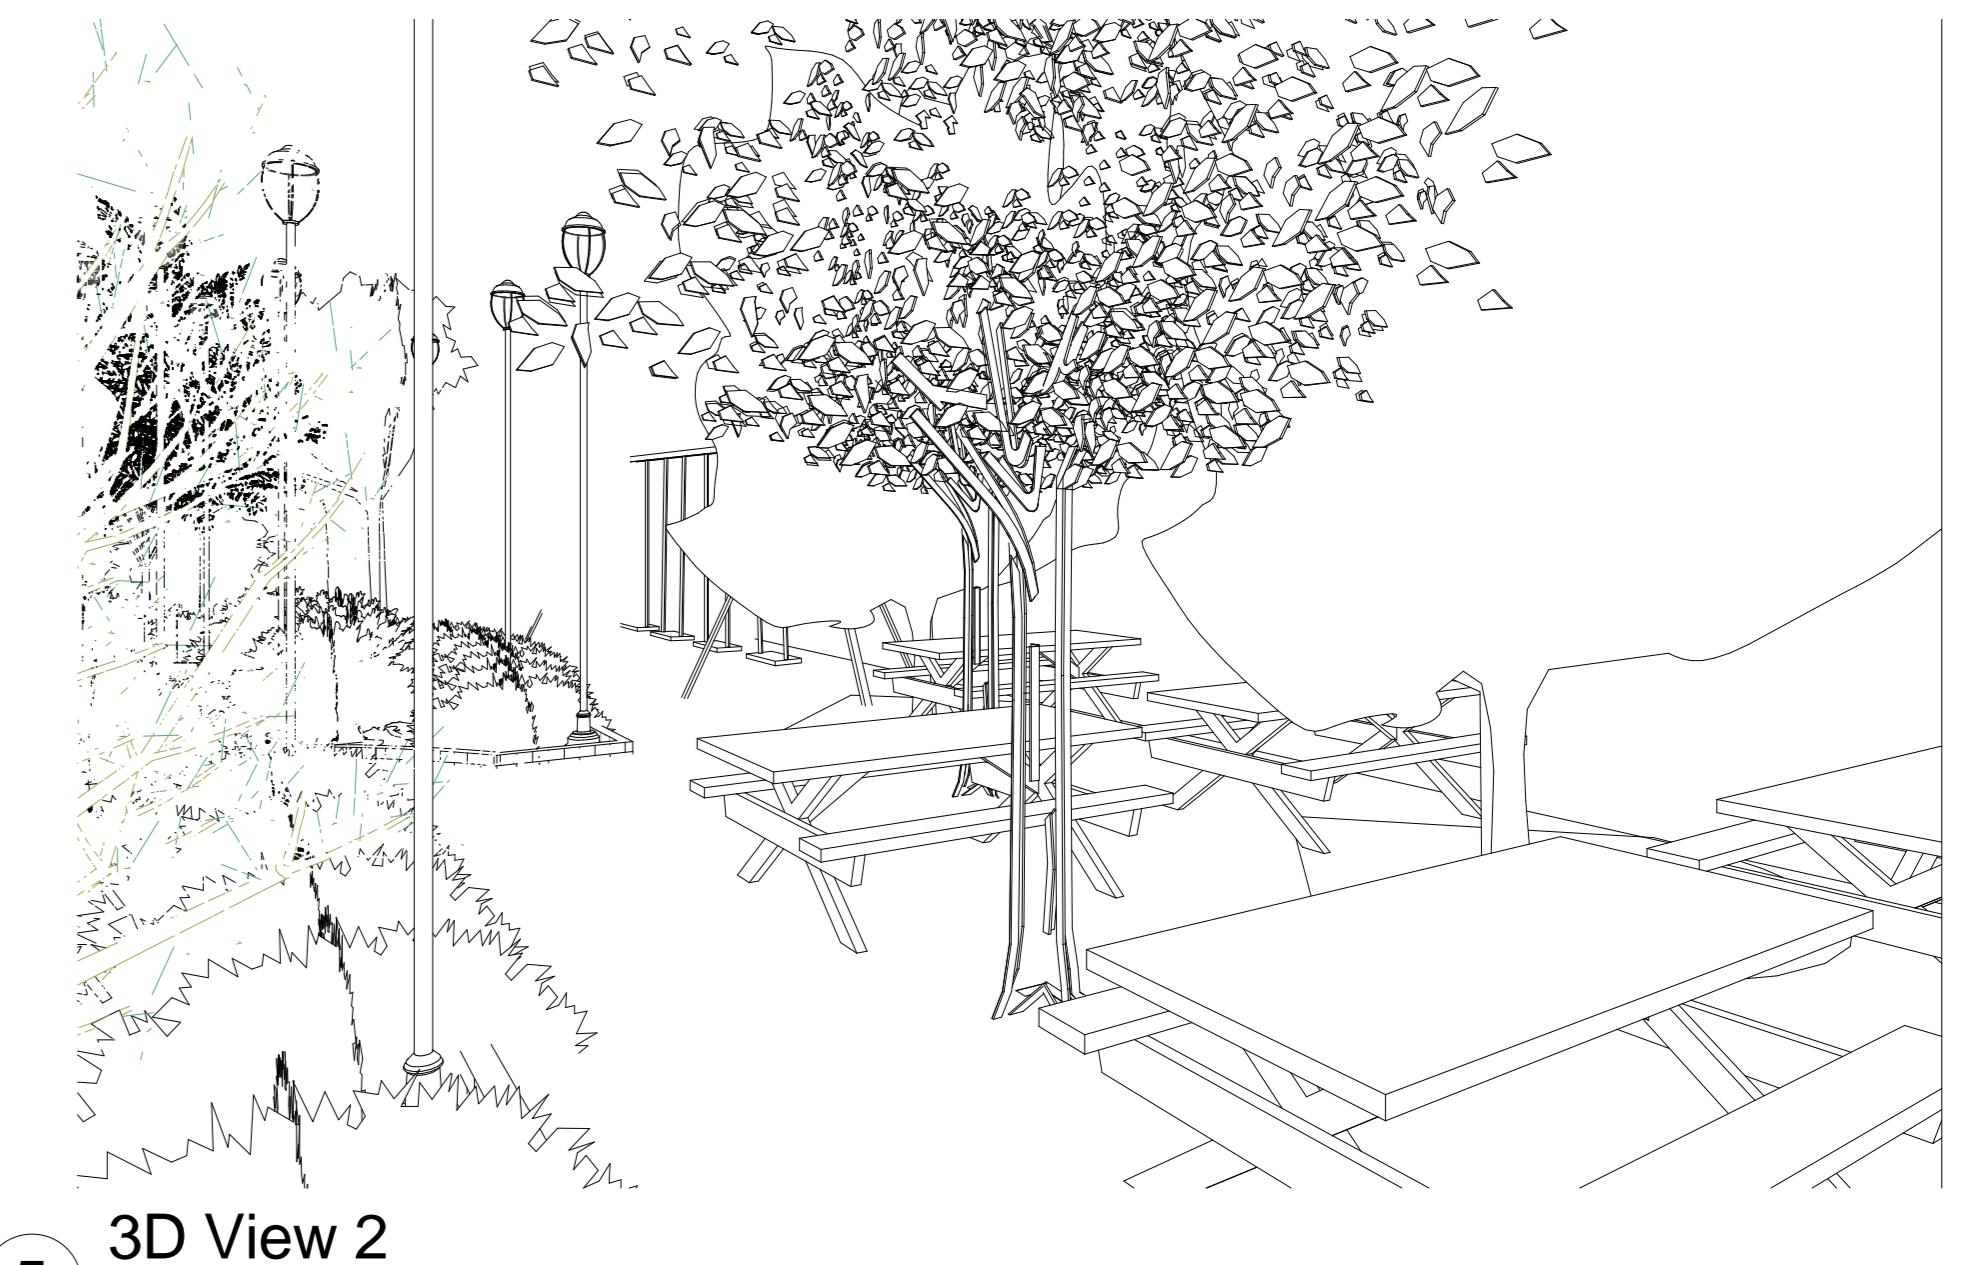


5 3D View 2



7 3D View 4



4 3D View 1

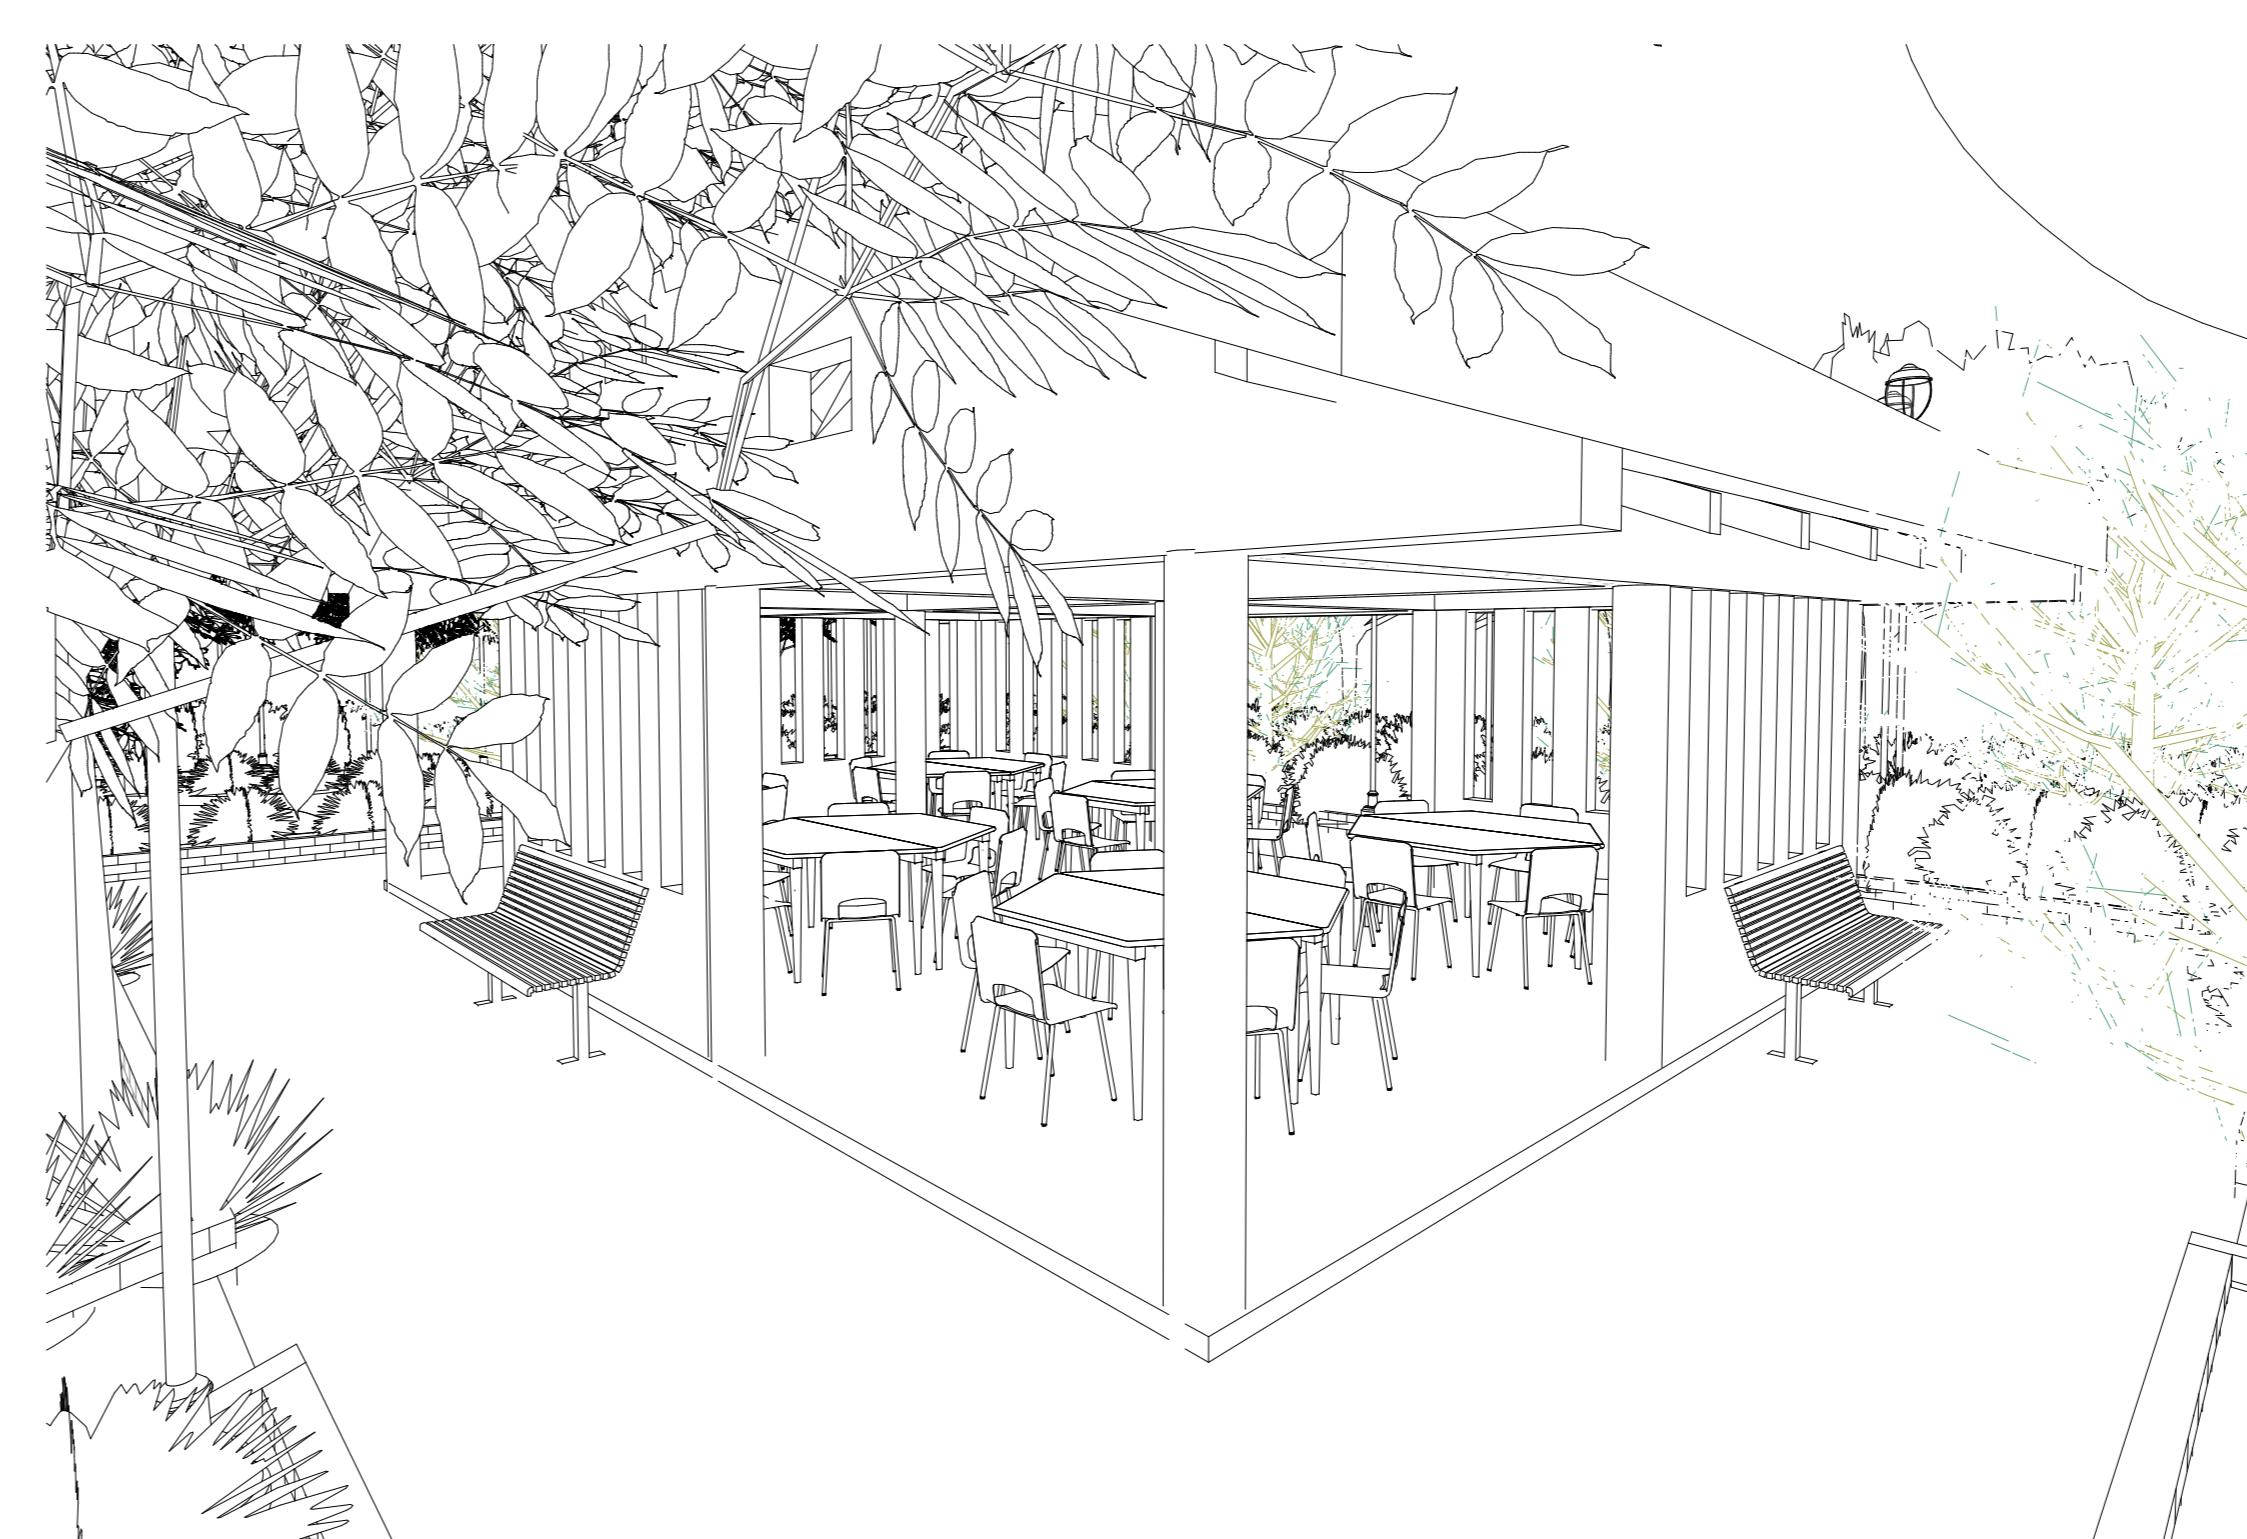

9 3D View 6



6 3D View 3

Facultad de Ingeniería Y  
Arquitectura  
Escuela de Arquitectura

Proyecto  
Remodelacion de un  
Ambiente Seco

Arquitectura y Ambiente  
Prof. Arq. Bichara Khoury  
Examen Especial

BR: Yessica Nolasco Rosario 100050293

Techo  
Isometrica

Escala  
1:50